
PŮDORYS 1NP · pracovní výkres pro stavbu

Podle 3D modelu v09 (index.html), výkresu D1.2 DSP (02/2024) a zaměřené desky 8,3 × 11,9 m. Obvodové otvory jsou okótované jako hrubý otvor ve zdivu (rám + 2 × 20 mm), výšky jsou od ±0,000 = hotová podlaha.

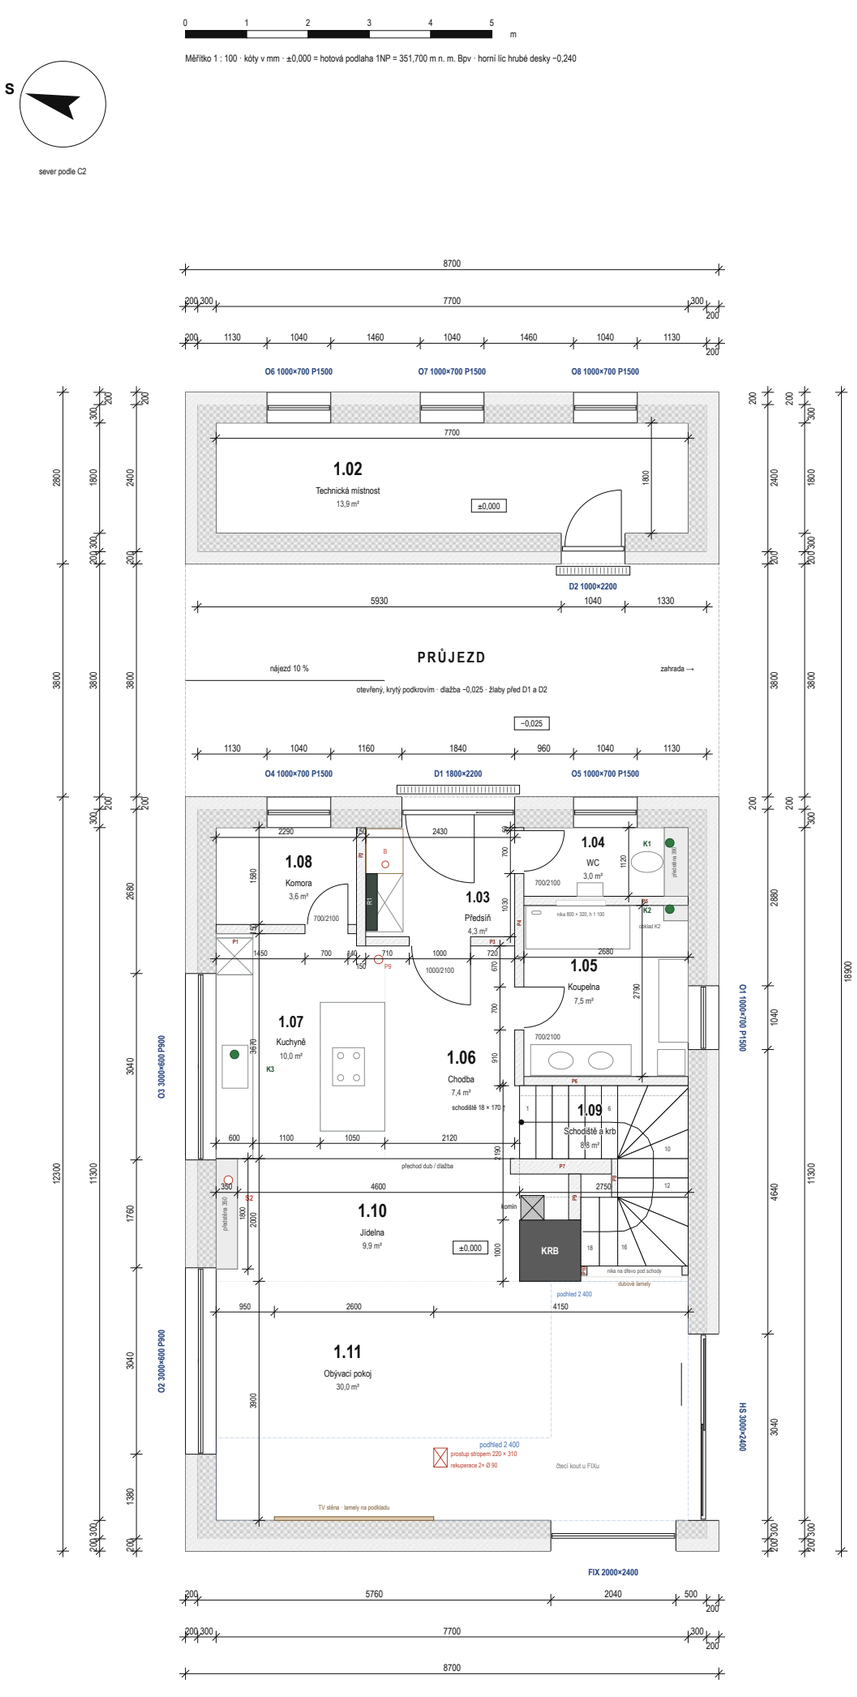

LEGENDA MÍSTNOSTÍ 1NP

Ozn.	Název	Plocha	D1.2	Podlaha
1.02	Technická místnost	13,9 m²	13 m²	dlažba
1.03	Předsíň	4,3 m²	5 m²	dlažba 60×120
1.04	WC	3,0 m²	3 m²	dlažba
1.05	Koupelna	7,5 m²	7 m²	dlažba
1.06	Chodba	7,4 m²	8 m²	dlažba 60×120
1.07	Kuchyně	10,0 m²	9 m²	dlažba 60×120
1.08	Komora	3,6 m²	4 m²	dlažba
1.09	Schodiště a krb	8,8 m²	5 m²	dub, schody dub
1.10	Jídelna	9,9 m²	9 m²	dub
1.11	Obývací pokoj	30,0 m²	29 m²	dub
1.01	Garáž	–	37 m²	vypuštěna
Celkem bez garáže		**98,3 m²**	**92 m²**	

Světlé plochy mezi omítnutými stěnami. Světlá výška 2 660 mm, v obýváku pod podhledem 2 400 mm (obrys čerchovaně). Hranice obýváku, jídelny, kuchyně a chodby jsou bez stěny (tečkovaně).

VÝPIS OTVORŮ V OBVODOVÝCH STĚNÁCH

Ozn.	Místo	Rám š × v	Otvor š	Parapet / práh	Vrch rámu	Překlad
FIX	přední štít u rohu, 1.11 pevné zasklení	2000 × 2400	2040	práh ±0	2400	2× IPE 240, L = 2 640 (300 + 2 040 + 300), uložení na ZB rohu potvrdit statikem
HS	boční stěna k terase, 1.11 zvedací posuvné, práh ±0	3000 × 2400	3040	práh ±0	2400	2× IPE 240, L 3 640 (300 na ZB rohu + 3 040 + 300)
O1	koupelna 1.05	1000 × 700	1040	P 1500	2200	SOLBET NS 140 (120 + 180)
O2	obýván 1.11 pevné zasklení v rámu, dvě pole se sloupkem	3000 × 600	3040	P 900	1500	2× IPE 240, L 3 640 (300 + 3 040 + 300)
O3	kuchyně 1.07 pevné zasklení v rámu, dvě pole se sloupkem; deska linky zajíždí do špalety jako parapet	3000 × 600	3040	P 900	1500	2× IPE 240, L 3 640 (300 + 3 040 + 300)
O4	komora 1.08	1000 × 700	1040	P 1500	2200	SOLBET NS 140 (120 + 180)
D1	vstup do předsíně 1.03 křídlo 1 200 + světlík 600 na straně WC, panty u světlíku	1800 × 2200	1840	práh ±0	2200	SOLBET NS 230 (120 + 180)
O5	WC 1.04	1000 × 700	1040	P 1500	2200	SOLBET NS 140 (120 + 180)
D2	vstup do technické 1.02 směr otevírání upřesnit	1000 × 2200	1040	práh ±0	2200	SOLBET NS 140 (120 + 180)
O6	technická 1.02	1000 × 700	1040	P 1500	2200	SOLBET NS 140 (120 + 180)
O7	technická 1.02	1000 × 700	1040	P 1500	2200	SOLBET NS 140 (120 + 180)
O8	technická 1.02	1000 × 700	1040	P 1500	2200	SOLBET NS 140 (120 + 180)

VNITŘNÍ DVEŘE

Ozn.	Křídlo š/v	Místo a otevírání
DV1	1000/2100	předsíň → chodba, otevírá do chodby, panty u WC
DV2	700/2100	chodba → koupelna, otevírá do koupelny, panty blíž ke vstupu
DV3	700/2100	chodba → WC, otevírá do WC, panty u obvodové stěny
DV4	700/2100	kuchyně → komora, skryté dveře v obkladu linky, otevírá do komory

Otvor v příčce je okótovaný podle modelu, upravit ho podle zvolené zárubně (obložková bývá o 50–100 mm širší než křídlo).

SKUTEČNÝ ROZMĚR PODLE DESKY

- **Deska je zaměřená na 8,3 × 11,9 m** a obvodové zdivo lícuje s její hranou. Zdivo domu je 8 300 × 11 900, technické 8 300 × 2 400, průjezd zůstává 4 200.
- Proti návrhu 8 000 × 12 000 jsou obě dlouhé stěny posunuté o 150 ven a vnitřní dispozice zůstala na místě (x + 150). Od s 9 600 je všechno o 100 blíž přednímu štítu, o 100 kratší jsou kuchyně, chodba a koupelna.
- Předpoklad: deska narostla o 150 na každou stranu. Hotové vývody K1–K3 (ZT02, stránka Kanalizace) jsou proto zakreslené jako návrh + 150, K1 a K2 jsou asi 300 od vnitřního líce pravé stěny místo 150. Předstěna WC je proto hluboká 390, aby v ní zůstaly K1 a V2, obklad K2 je hlubký 400. Před zděním příček vývody zaměřit.
- Stropní panely jsou nově dlouhé 7 950 (rozpětí 7 700), potvrdit statikem.

ZB roh 300 × 500 (ztracené bednění, beton):
x 7 800–8 300, s 0–300. Mezi FIX a HS není tvárnice.
FIX: rám x 5 780–7 780, hrubý otvor 5 760–7 800.
HS: rám s 320–3 320, hrubý otvor 300–3 340.
Rámy u vnějšího líce zdiva (10–85 mm), EPS 200 přes rám.
Vnitřní líc pilíře mezi ostěními je jen 200 mm.
Nad oběma otvory 2× IPE 240; uložení na ZB rohu
a spojení párů IPE potvrdit statikem.

ZMĚNY PROTI D1.2 (POVOLENÍ)

1. **Dům 8 300 × 11 900** podle zaměřené desky: o 300 širší a o 70 delší než zdivo v DSP (8 000 × 11 830), hřeben o 150 výš.
2. Bez garáže 1.01. Technická místnost 1.02 zůstává za otevřeným průjezdem (8 300 × 2 400).
3. **HS 3 000 × 2 400** hned u předního rohu (D1.2: HS 2 000 × 2 200 ve vzdálenosti 1 420 od rohu a dveře 1 000 × 2 200 u schodiště, ty jsou zrušené).
4. **FIX 2 000 × 2 400** v předním štítu u stejného rohu, roh ze ZB 300 × 500 (D1.2: tři francouzská okna 1 000 × 2 200 ve štítu).
5. Okna O2, O3 **3 000 × 600, P 900** (D1.2: 3 000 × 900, P 900). Poloha beze změny. Obě **pevně zasklená**.
6. Vstup D1 ve stejném otvoru 1 800, nově křídlo 1 200 + světlík 600. Dveře předsíň → chodba jednokřídlé 1 000 v ose vstupu (D1.2: 1 600 dvoukřídlé).
7. Příčka předsíň a chodba / WC a koupelna má líc na 5 170 (D1.2: 5 100, po rozšíření domu 5 250). Světlík pak končí v rohu u WC, předsíň a chodba jsou o 80 mm užší, WC a koupelna o 80 mm širší. Pokud chceš držet D1.2, posuň příčku a oboje dveře o 80 mm.
8. Koupelna bez pračky a sušičky (jsou v podkroví 2.05), vana se zástěnou, skříňka pod oknem. Nad vanou nika 800 × 320 v příčce P5 (80 do tvárnice), umývátko ve WC proto se stojánkovou baterií. Stoupačka K2 v rohu obložená. WC s předstěnou 390 přes čelo, schová K1 a V2 (D1.2: předstěna 165 podél obvodové stěny).
9. Schodiště 18 × 170 mm, konstrukční výška 3 060 podle výškového řezu (D1.2: 18 × 166,7). Výroba podle zaměření.
10. Pilíř mezi O2 a O3: předstěna 350 se stoupačkou S2 do K3 (Kanalizace, varianta A).
11. **Příčka P1 kuchyně / komora o 200 dál v komoře** (D1.2: v linii s P3), aby se za okno O3 vešla vestavná lednice 600 a distanční lišta pro dveře přes 90°. Kuchyně je o 100 kratší, na lištu zbývá 70 místo 170; ověřit, případně P1 o 100 dál. Komora 1 580 místo 1 780, ostrůvek od skrytých dveří 1 050.
12. Krb v rohu schodiště, k obýváku dubové lamely a nika na dřevo pod posledními stupni.

POZNÁMKY

- Pracovní výkres z vizualizační studie, ne realizační dokumentace. Před zděním kóty zkontrolovat na desce a vůči vývodům K1–K3.
- Nosné prvky podle statiky (Ing. Khol, 04/2024): překlady 2× IPE 240, ZB roh FIX–HS, uložení panelů a výměna u schodiště. Délky IPE ověřit před objednáním.
- Prostup stropem 220 × 310 (x 3 850–4 070, s 1 170–1 480) pro dvě trubky rekuperace Ø 90 z kastlíku na předním konci dělicí stěny ložnice: vývrt do dutin panelu uprostřed rozpětí, musí být na výrobním výkresu panelů.
- Prostup P9 Ø 140 ve stropě kuchyně u dveří do předsíně (x 2 950, s 9 450) pro odvod kuchyně Ø 125 svisle do skříně pokoje 2.04 k V3. Do výrobního výkresu panelů spolu s ostatními (stránky Rekuperace a Stropní panely).
- R1 = rozdělovač podlahovky ve vestavěné skříni, B = stoupačka topení R2 → R1 a chráničky, nad sedací nikou v instalačním pásu Z2 (s 11 000). R-A (elektrorozvaděč) je v D1.2 na stěně u komory vedle vstupu, kde je teď sedací nika. Polohu sladit s PD elektro.
- Zárubeň DV3 (WC) je jen 50 mm od rohu. Ověřit podle typu zárubně, případně dveře posunout o 100 mm.
- Změny vnějších otvorů, rozměr domu a vypuštění garáže projednat se stavebním úřadem (změna stavby před dokončením).

VYTYČENÍ PŘÍČEK


Ozn.	Mezi	x	s	Tl.	Kontrola	Otvory
P1	kuchyně / komora	300–2 590	9 870–10 020	150	1 580 od vnitřního líce vstupní stěny	DV4 700, 1 450 od levé stěny
P2	komora / předsíň	2 590–2 740	9 670–11 600	150	2 290 od vnitřního líce levé stěny	
P3	předsíň / chodba	2 740–5 170	9 670–9 820	150	200 před P1 (P1 je kvůli lednici posunutá do komory)	DV1 1 000, 710 od P2
P4	chodba / koupelna a WC	5 170–5 320	7 390–11 600	150	2 680 od vnitřního líce pravé stěny	DV2 700, 910 od P6 · DV3 700, 50 od vstupní stěny
P5	koupelna / WC	5 320–8 000	10 330–10 480	150	1 120 od vnitřního líce vstupní stěny	nika nad vanou 800 × 320, x 5 850–6 650, 1 100–1 420 nad hotovou podlahou, 80 do tvárnice ze strany koupelny
P6	schodiště / koupelna	5 320–8 000	7 390–7 540	150	2 790 od P5	
P7	pod 1. ramenem, ke krbu, nosná pod VM2	5 100–6 750	5 950–6 200	250	konec 150 před prvním stupněm	
P8	střední stěna schodiště	6 750–6 850	5 570–6 200	100		
P9	komín / schodiště, nosná pod VM1	6 050–6 250	5 200–5 950	200		
P10	pilířky u niky na dřevo	6 250–6 350, 7 900–8 000	4 300–4 450	100		mezi nimi dubové lamely

x od vnějšího líce zdiva na straně přijezdu, s od vnějšího líce zdiva předního štítu, stejně jako na stránce První řada zdiva. Kontrolní míra je k líci příčky na straně uvedené místnosti.

LEGENDA MATERIÁLŮ

- nosné zdivo SOLBET 590 × 240 × 300 na tenkovrstvé lepidlo
- EPS 200 (fasáda)
- železobeton (ZB roh FIX–HS), komín
- příčka pórobeton 150 (střední stěna schodiště 100, nosné P7 250 a P9 200)
- předstěna, obklad stoupačky (SDK)
- K1–K3 hotové vývody DN 110 · S2 nová stoupačka
- otvor ve stropě nad schodištěm
- snížený podhled, světlá výška 2 400
- hranice místností bez stěny

DETAIL ROHU FIX–HS · 1 : 20

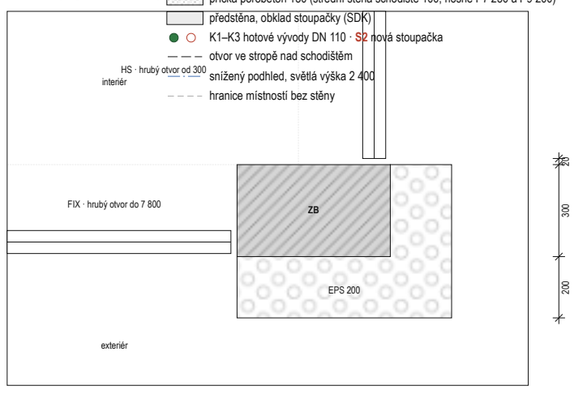

Stavba	**Novostavba rodinného domu Hájek** · p. p. č. 49/5, k. ú. Krásný Les u Frýdlantu		
Investor	Ing. Luboš Hájek	Měřítko	1 : 100 (A3)
Podklady	D1.2 DSP (Ing. Dávid Jurčo, 02/2024), statika Ing. Khol 04/2024, 3D studie v09, Kanalizace, Topení, zaměření desky	Datum	3. 11. 2026
Zpracoval	— Claude (AI asistent)	Výkres	**Půdorys 1NP**