
PŮDORYS 1NP · pracovní výkres pro stavbu

Podle 3D modelu v09 (index.html) a výkresu D1.2 DSP (02/2024). Obvodové otvory jsou okótované jako hrubý otvor ve zdivu (rám + 2 × 20 mm), výšky jsou od ±0,000 = hotová podlaha.

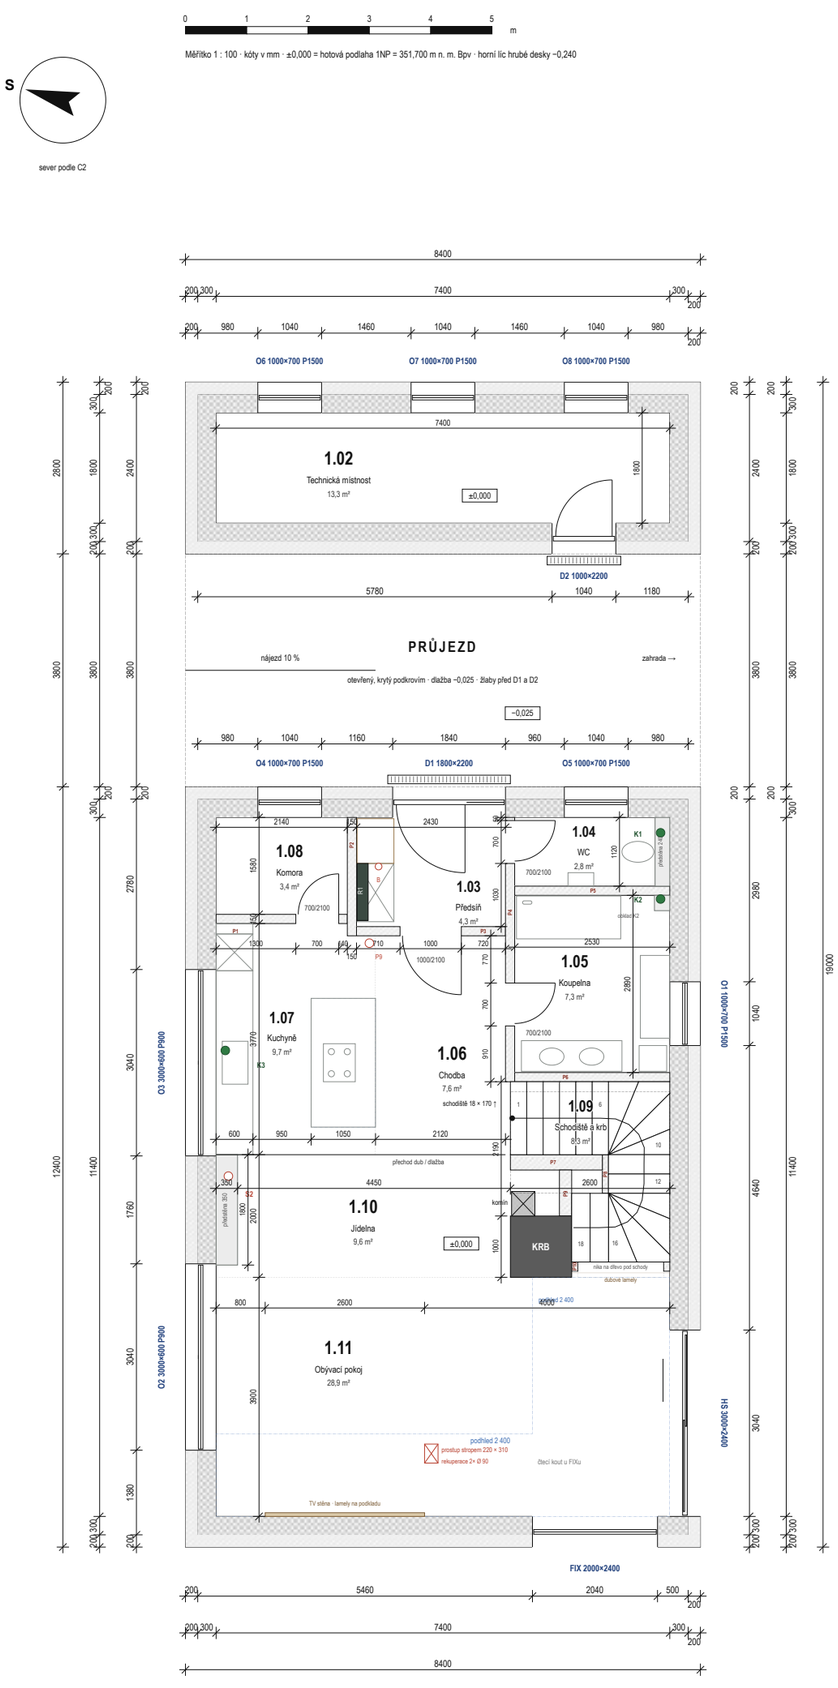

LEGENDA MÍSTNOSTÍ 1NP

Ozn.	Název	Plocha	D1.2	Podlaha
1.02	Technická místnost	13,3 m²	13 m²	dlažba
1.03	Předsíň	4,3 m²	5 m²	dlažba 60×120
1.04	WC	2,8 m²	3 m²	dlažba
1.05	Koupelna	7,3 m²	7 m²	dlažba
1.06	Chodba	7,6 m²	8 m²	dlažba 60×120
1.07	Kuchyně	9,7 m²	9 m²	dlažba 60×120
1.08	Komora	3,4 m²	4 m²	dlažba
1.09	Schodiště a krb	8,3 m²	5 m²	dub, schody dub
1.10	Jídelna	9,6 m²	9 m²	dub
1.11	Obývací pokoj	28,9 m²	29 m²	dub
1.01	Garáž	–	37 m²	vypuštěna
Celkem bez garáže		**95,2 m²**	**92 m²**	

Světlé plochy mezi omítnutými stěnami. Světlá výška 2 660 mm, v obýváku pod podhledem 2 400 mm (obrys čerchovaně). Hranice obýváku, jídelny, kuchyně a chodby jsou bez stěny (tečkované).

VÝPIS OTVORŮ V OBVODOVÝCH STĚNÁCH

Ozn.	Místo	Rám š × v	Otvor š	Parapet / práh	Vrch rámu	Překlad
FIX	přední štít u rohu, 1.11 pevné zasklení	2000 × 2400	2040	práh ±0	2400	2× IPE 240, L ≈ 2 500 (podle nákupu), uložení na ZB rohu potvrdit statikem
HS	boční stěna k terase, 1.11 zvedací posuvné, práh ±0	3000 × 2400	3040	práh ±0	2400	2× IPE 240, L 3 640 (statika Ing. Khol)
O1	koupelna 1.05	1000 × 700	1040	P 1500	2200	SOLBET NS 140 (120 + 180)
O2	obýván 1.11	3000 × 600	3040	P 900	1500	2× IPE 240, L 3 500
O3	kuchyně 1.07 deska linky zajíždí do špalety jako parapet	3000 × 600	3040	P 900	1500	2× IPE 240, L 3 500
O4	komora 1.08	1000 × 700	1040	P 1500	2200	SOLBET NS 140 (120 + 180)
D1	vstup do předsíně 1.03 křídlo 1 200 + světlík 600 na straně WC, panty u světlíku	1800 × 2200	1840	práh ±0	2200	SOLBET NS 230 (120 + 180)
O5	WC 1.04	1000 × 700	1040	P 1500	2200	SOLBET NS 140 (120 + 180)
D2	vstup do technické 1.02 směr otevírání upřesnit	1000 × 2200	1040	práh ±0	2200	SOLBET NS 140 (120 + 180)
O6	technická 1.02	1000 × 700	1040	P 1500	2200	SOLBET NS 140 (120 + 180)
O7	technická 1.02	1000 × 700	1040	P 1500	2200	SOLBET NS 140 (120 + 180)
O8	technická 1.02	1000 × 700	1040	P 1500	2200	SOLBET NS 140 (120 + 180)

VNITŘNÍ DVEŘE

Ozn.	Křídlo š/v	Místo a otevírání
DV1	1000/2100	předsíň → chodba, otevírá do chodby, panty u WC
DV2	700/2100	chodba → koupelna, otevírá do koupelny, panty blíž ke vstupu
DV3	700/2100	chodba → WC, otevírá do WC, panty u obvodové stěny
DV4	700/2100	kuchyně → komora, skryté dveře v obkladu linky, otevírá do komory

Otvor v příčce je okótovaný podle modelu, upravit ho podle zvolené zárubně (obložková bývá o 50–100 mm širší než křídlo).

ZMĚNY PROTI D1.2 (POVOLENÍ)

1. Bez garáže 1.01. Technická místnost 1.02 zůstává za otevřeným průjezdem (8 000 × 2 400).
2. **HS 3 000 × 2 400** hned u předního rohu (D1.2: HS 2 000 × 2 200 ve vzdálenosti 1 420 od rohu a dveře 1 000 × 2 200 u schodiště, ty jsou zrušené).
3. **FIX 2 000 × 2 400** v předním štítu u stejného rohu, roh ze ZB 300 × 500 (D1.2: tři francouzská okna 1 000 × 2 200 ve štítu).
4. Okna O2, O3 **3 000 × 600, P 900** (D1.2: 3 000 × 900, P 900). Poloha beze změny.
5. Vstup D1 ve stejném otvoru 1 800, nově křídlo 1 200 + světlík 600. Dveře předsíň → chodba jednokřídlé 1 000 v ose vstupu (D1.2: 1 600 dvoukřídlé).
6. Příčka předsíň a chodba / WC a koupelna má líc na 5 020 (D1.2: 5 100). Světlík pak končí v rohu u WC, předsíň a chodba jsou o 80 mm užší, WC a koupelna o 80 mm širší. Pokud chceš držet D1.2, posuň příčku a oboje dveře o 80 mm.
7. Koupelna bez pračky a sušičky (jsou v podkroví 2.05), vana se zástěnou, skříňka pod oknem. Stoupačka K2 v rohu obložená. WC s předstěnou 240 přes čelo (D1.2: předstěna 165 podél obvodové stěny).
8. Schodiště 18 × 170 mm, konstrukční výška 3 060 podle výškového řezu (D1.2: 18 × 166,7). Výroba podle zaměření.
9. Pilíř mezi O2 a O3: předstěna 350 se stoupačkou S2 do K3 (Kanalizace, varianta A).
10. **Příčka P1 kuchyně / komora o 200 dál v komoře** (D1.2: v linii s P3). V rohu kuchyně se tak vejde vestavná lednice 600 hned za oknem O3 a distanční lišta 170 u stěny, aby šly dveře přes 90°. Komora má 1 580 místo 1 780, ostrůvek je od skrytých dveří 1 150.
11. Krb v rohu schodiště, k obýváku dubové lamely a nika na dřevo pod posledními stupni.

POZNÁMKY

- Pracovní výkres z vizualizační studie, ne realizační dokumentace. Před zděním kóty zkontrolovat na desce a vůči vývodům K1–K3.
- Nosné prvky podle statiky (Ing. Khol, 04/2024): překlady 2× IPE 240, ZB roh FIX–HS, uložení panelů a výměna u schodiště. Délky IPE ověřit před objednáním.
- Prostup stropem 220 × 310 (x 3 700–3 920, s 1 170–1 480) pro dvě trubky rekuperace Ø 90 z kastlíku na předním konci dělicí stěny ložnice: vývrt do dutin panelu uprostřed rozpětí, musí být na výrobním výkresu panelů.
- Prostup P9 Ø 140 ve stropě kuchyně u dveří do předsíně (x 2 800, s 9 650) pro odvod kuchyně Ø 125 svisle do skříně pokoje 2.04 k V3. Do výrobního výkresu panelů spolu s ostatními (stránka Rekuperace).
- Vývody K1–K3 jsou v desce hotové (ZT02, stránka Kanalizace). Před zděním příček je zaměřit.
- R1 = rozdělovač podlahovky ve vestavěné skříni, B = stoupačka topení R2 → R1 a chráničky. R-A (elektrorozvaděč) je v D1.2 na stěně u komory vedle vstupu, kde je teď sedací nika. Polohu sladit s PD elektro.
- Zárubeň DV3 (WC) je jen 50 mm od rohu. Ověřit podle typu zárubně, případně dveře posunout o 100 mm.
- Změny vnějších otvorů a vypuštění garáže projednat se stavebním úřadem (změna stavby před dokončením).

VYTYČENÍ PŘÍČEK

Ozn.	Mezi	x	s	Tl.	Kontrola	Otvory
P1	kuchyně / komora	300–2 440	9 970–10 120	150	1 580 od vnitřního líce vstupní stěny	DV4 700, 1 300 od levé stěny
P2	komora / předsíň	2 440–2 590	9 770–11 700	150	2 140 od vnitřního líce levé stěny	
P3	předsíň / chodba	2 590–5 020	9 770–9 920	150	200 před P1 (P1 je kvůli lednici posunutá do komory)	DV1 1 000, 710 od P2
P4	chodba / koupelna a WC	5 020–5 170	7 390–11 700	150	2 530 od vnitřního líce pravé stěny	DV2 700, 910 od P6 · DV3 700, 50 od vstupní stěny
P5	koupelna / WC	5 170–7 700	10 430–10 580	150	1 120 od vnitřního líce vstupní stěny	
P6	schodiště / koupelna	5 170–7 700	7 390–7 540	150	2 890 od P5	
P7	pod 1. ramenem, ke krbu	5 100–6 600	5 950–6 200	250		
P8	střední stěna schodiště	6 600–6 700	5 570–6 200	100		
P9	komín / schodiště, nosná pod VM1	5 900–6 100	5 200–5 950	200		
P10	pilířky u niky na dřevo	6 100–6 200, 7 600–7 700	4 300–4 450	100		mezi nimi dubové lamely


x od vnějšího líce zdiva na straně příjezdu, s od vnějšího líce zdiva předního štítu, stejně jako na stránce První řada zdiva. Kontrolní míra je k líci příčky na straně uvedené místnosti.

LEGENDA MATERIÁLŮ

- nosné zdivo SOLBET 590 × 240 × 300 na tenkovrstvé lepidlo
- EPS 200 (fasáda)
- železobeton (ZB roh FIX–HS), komín
- příčka pórobeton 150 (stěny schodiště 100 a 250, nosná P9 200)
- předstěna, obklad stoupačky (SDK)
- K1–K3 hotové vývody DN 110 · S2 nová stoupačka
- otvor ve stropě nad schodištěm
- snížený podhled, světlá výška 2 400
- hranice místností bez stěny

ZB roh 300 × 500 (ztracené bednění, beton):
x 7 500–8 000, s 0–300. Mezi FIX a HS není tvárnice.
FIX: rám x 5 480–7 480, hrubý otvor 5 460–7 500.
HS: rám s 320–3 320, hrubý otvor 300–3 340.
Rámy u vnějšího líce zdiva (10–85 mm), EPS 200 přes rám.
Vnitřní líc pilíře mezi ostěními je jen 200 mm.
Nad oběma otvory 2× IPE 240; uložení na ZB rohu
a spojení párů IPE potvrdit statikem.

DETAIL ROHU FIX–HS · 1 : 20

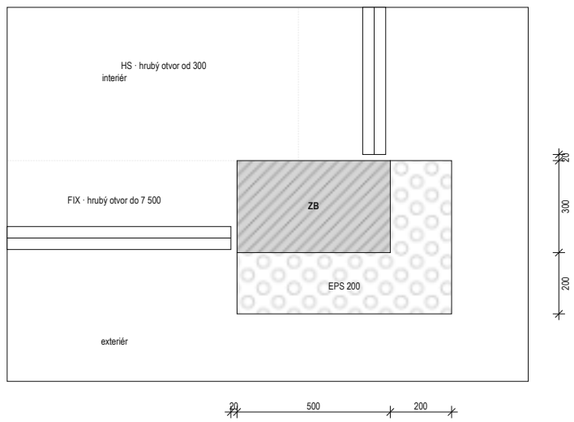

Stavba	**Novostavba rodinného domu Hájek** · p. p. č. 49/5, k. ú. Krásný Les u Frýdlantu		
Investor	Ing. Luboš Hájek	Měřítko	1 : 100 (A3)
Podklady	D1.2 DSP (Ing. Dávid Jurčo, 02/2024), statika Ing. Khol 04/2024, 3D studie v09, Kanalizace, Topení	Datum	20. 10. 2026
Zpracoval	— Claude (AI asistent)	Výkres	**Půdorys 1NP**